


House plan from your sketch: every number is an editable box, in cm

Grey text under a box = what the sketch says. Numbers without 'cm' were taken as inches and converted (x 2.54). '?' = unclear reading: please check.

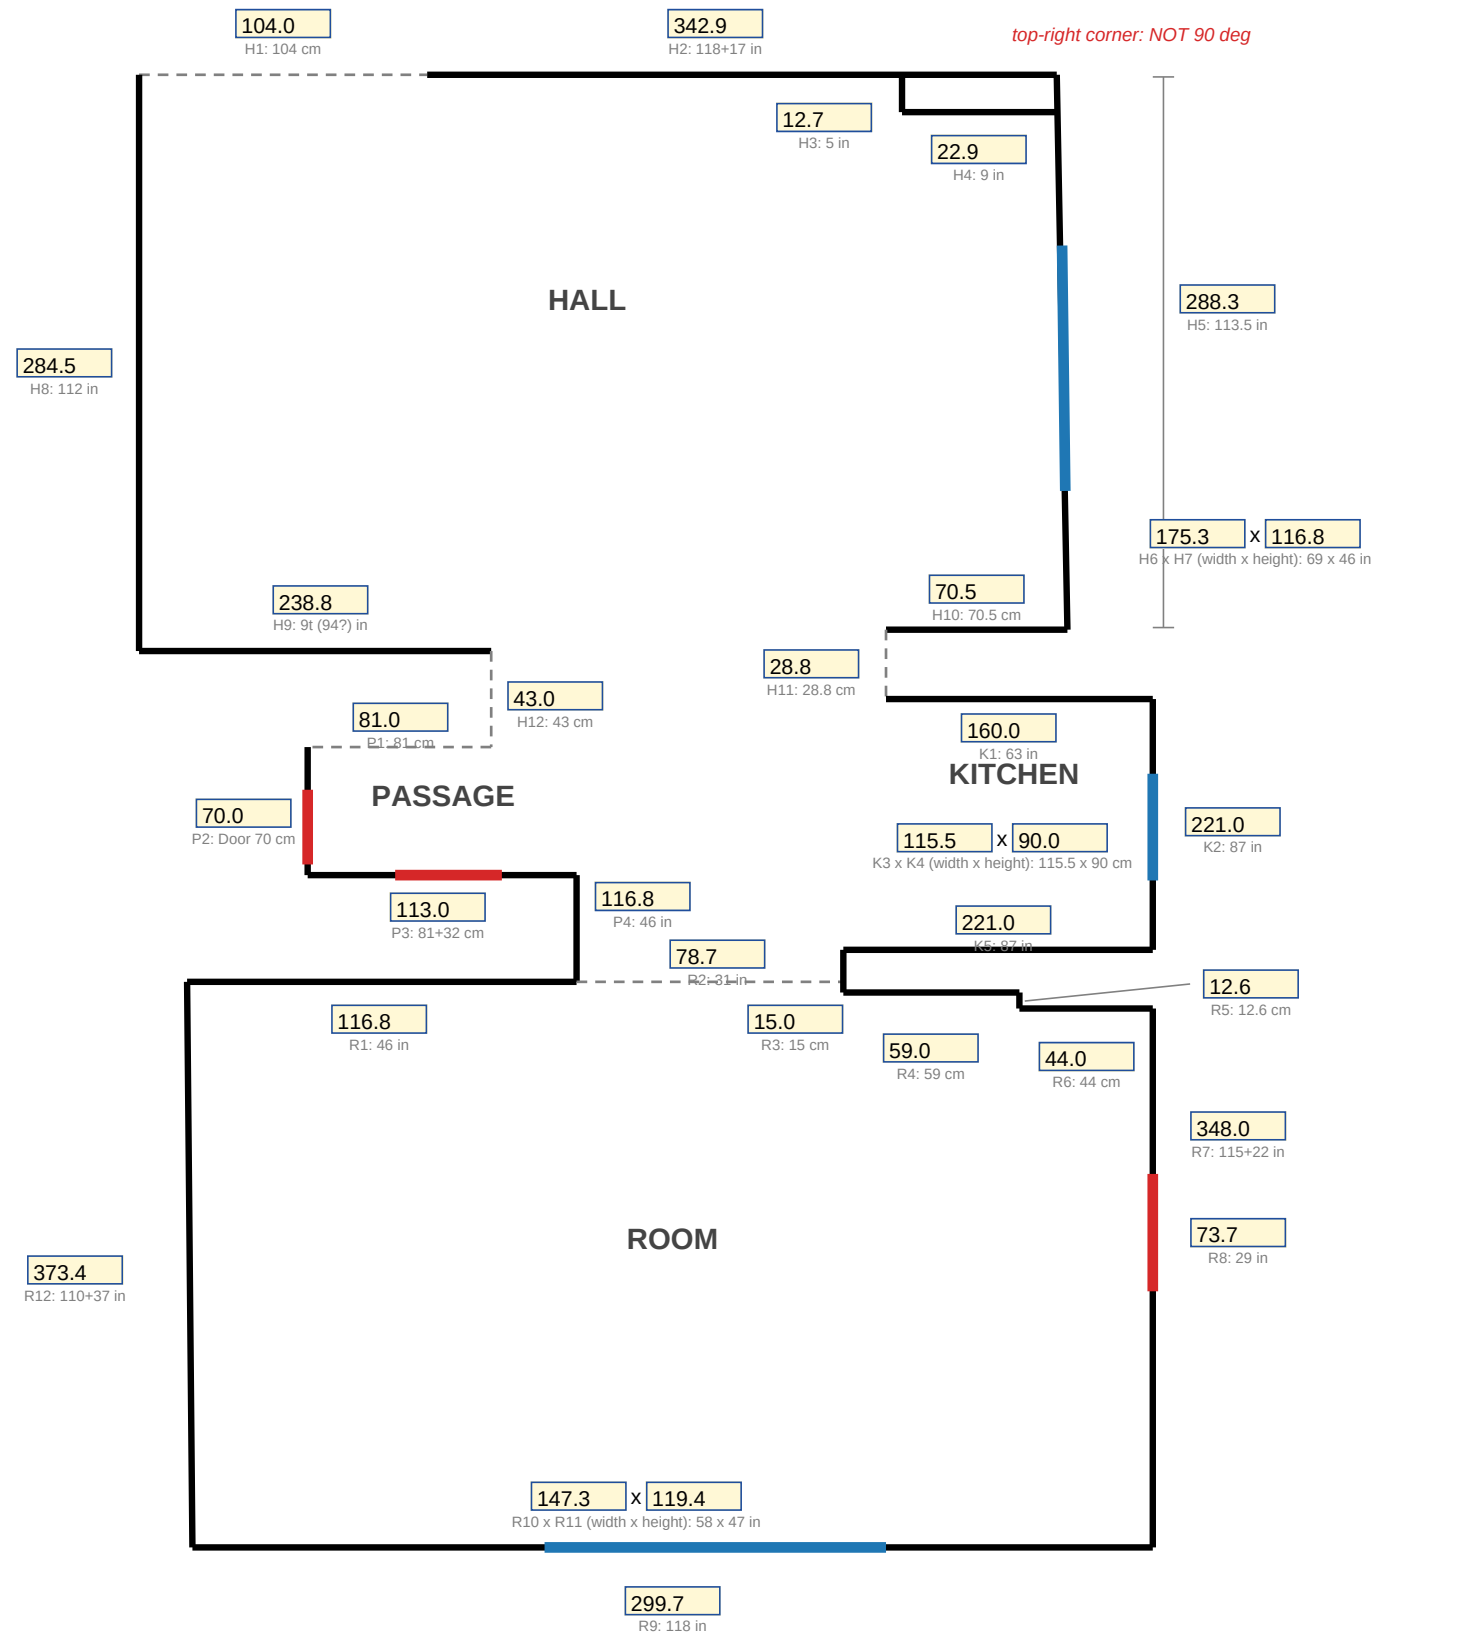


Legend — wall - - - open / no wall (dashed) ■ window ■ door

Notes from you: in the ROOM the lengths leave out the beams (columns), and the small recesses on both sides of the window wall. The scoring will adjust for that. Hall: the top-right corner is not 90 deg.
Check: Room top wall R1+R2+R4+R6 = 298.5 cm against bottom wall R9 = 299.7 cm (difference 1.2 cm).
Room left wall R12 = 373.4 cm, right wall R7 = 348.0 cm: 25.4 cm apart (the top wall steps, R3/R5?). Please confirm.
Drawing is a clean copy of your sketch's layout, not to scale. Page 2: your sketch. Page 3: every value in a table.

Your corrections / comments:

Your sketch (reference)

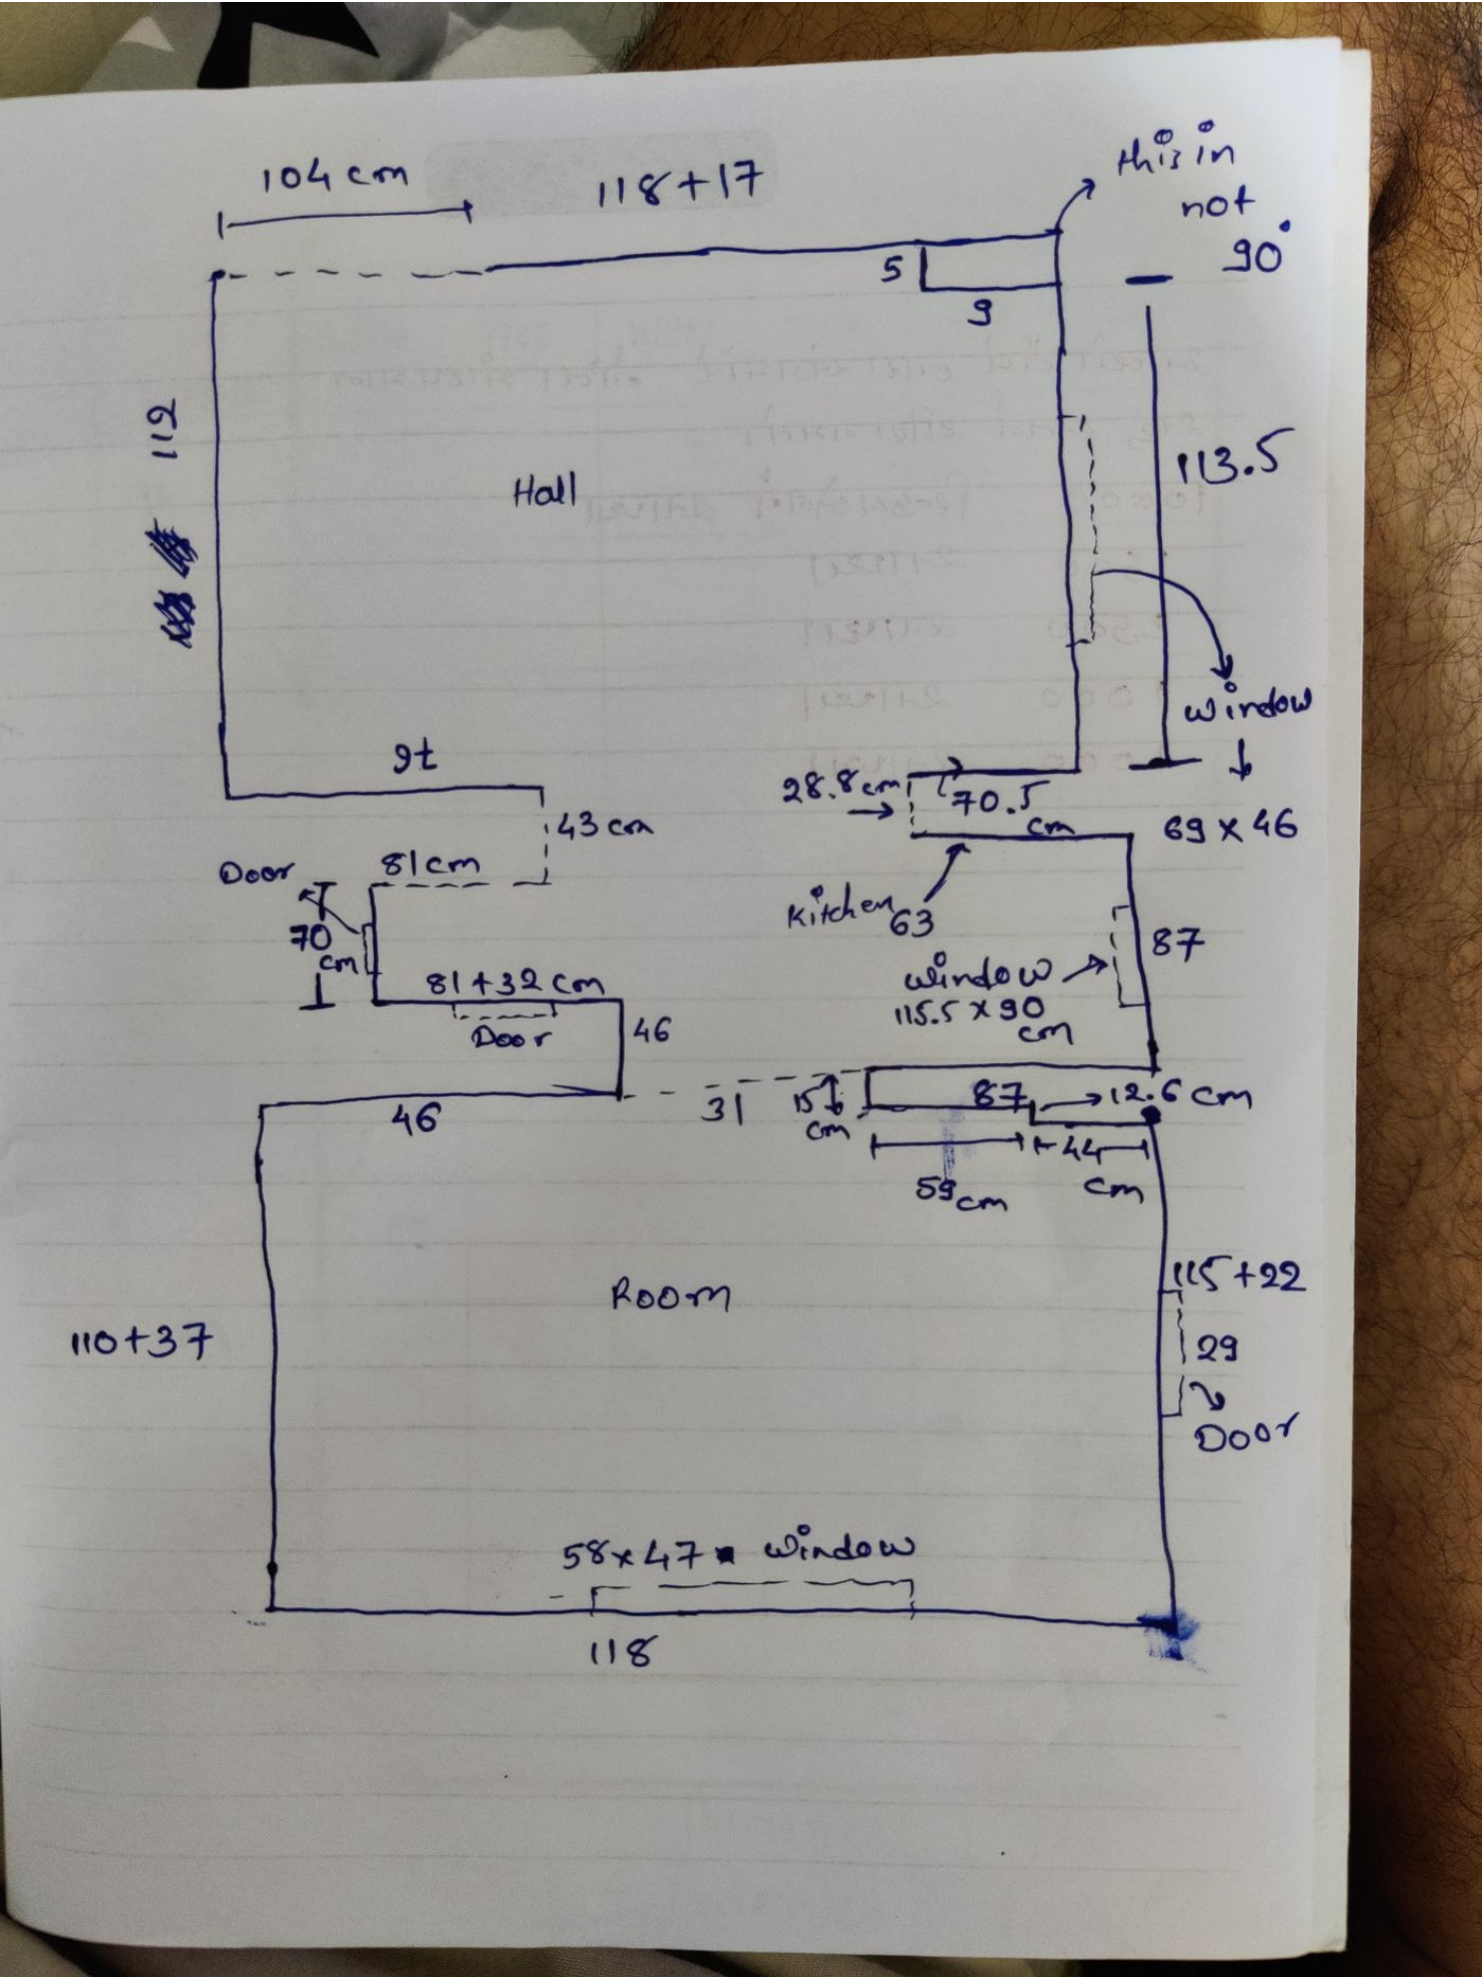

Every measurement (the editable boxes are on page 1)

ID	Room	What	Sketch says	Unit	cm
H1	Hall	top wall, open part on the left (dashed)	104 cm	cm	104.0
H2	Hall	top wall, solid part	118+17	inch	342.9
H3	Hall	column at top-right corner, depth	5	inch	12.7
H4	Hall	column at top-right corner, width	9	inch	22.9
H5	Hall	right wall (window wall)	113.5	inch	288.3
H6	Hall	window on right wall, width	69 (x 46)	inch	175.3
H7	Hall	window on right wall, height	(69 x) 46	inch	116.8
H8	Hall	left wall	112	inch	284.5
H9	Hall	bottom wall, left part (read as '9t' = 94?)	9t (94?)	inch	238.8
H10	Hall	bottom wall, right part (next to kitchen)	70.5 cm	cm	70.5
H11	Hall	step down to the kitchen top wall (dashed)	28.8 cm	cm	28.8
H12	Hall	dashed drop at the end of the bottom-left wall	43 cm	cm	43.0
P1	Passage	opening from the hall side (dashed)	81 cm	cm	81.0
P2	Passage	left wall: door	Door 70 cm	cm	70.0
P3	Passage	bottom wall (with a door)	81+32 cm	cm	113.0
P4	Passage	right side, down to the room's top wall	46	inch	116.8
R1	Room	top wall, left part	46	inch	116.8
R2	Room	door on top wall (dashed)	31	inch	78.7
R3	Room	wall thickness, kitchen-room wall	15 cm	cm	15.0
R4	Room	top wall, right part 1 (below kitchen)	59 cm	cm	59.0
R5	Room	step in top wall	12.6 cm	cm	12.6
R6	Room	top wall, right part 2	44 cm	cm	44.0
R7	Room	right wall	115+22	inch	348.0
R8	Room	door on right wall	29	inch	73.7
R9	Room	bottom wall (window wall)	118	inch	299.7
R10	Room	window on bottom wall, width	58 (x 47)	inch	147.3
R11	Room	window on bottom wall, height	(58 x) 47	inch	119.4
R12	Room	left wall	110+37	inch	373.4
K1	Kitchen	top wall	63	inch	160.0
K2	Kitchen	right wall (window wall)	87	inch	221.0
K3	Kitchen	window on right wall, width	115.5 cm (x 90)	cm	115.5
K4	Kitchen	window on right wall, height	(115.5 x) 90 cm	cm	90.0
K5	Kitchen	bottom wall (kitchen side)	87	inch	221.0